CONCEPT 2 — MULTIGENERATIONAL HOUSE

Two storeys · drive-through west carport · central skylight stair + reserved lift · ground-floor suite for the older couple



Blender render — street view (golden hour)

A two-storey multigenerational house for three generations. A covered drive-through carport and service bay runs down the west side, open to the road at the front and to the garden at the back. The entrance hall (Huyền Quan) opens to a central stair under a skylight, with a 1.6 × 1.6 m shaft beside it reserved for a future lift. The ground floor works on its own for the older couple: a master suite, an accessible bathroom and a flexible room that can become a bedroom or study. Living and dining face the north garden through large openings, with the kitchen and a compact wet kitchen beside them. Upstairs there are three bedrooms for the daughter's family, a family lounge and a shaded north balcony. The east wall is blank against the assumed 3-storey neighbour. Nothing is built on the DNN land except the boundary walls down to the water.



Concept 2 brief image (inspiration)

THE CONCEPT IN NUMBERS


Footprint	158.4 m² (60% of ONT band)
Ground floor	158 m² enclosed
Upper floor	137 m² enclosed + 21 m² balcony
Total enclosed	296 m²
Constraint check	PASS — all structures in ONT; DNN planting only

Walkthrough test: 21/21 rooms reachable


The brief asks for a 3.3–3.6 m drive-through carport plus a full house inside the 13.5 m ONT frontage. That leaves a 9.6 m wide house, kept back 0.3 m from the east party wall so the eaves stay on the plot. The future lift shaft (1.6 × 1.6 m) is reserved on both floors next to the stair, so a lift can go in later without structural changes. The carport is open at both ends; driving out to the garden crosses DNN land as access only, with no paving or structure there.

CONCEPT ONLY — NOT FOR CONSTRUCTION · subject to survey, legal merger, setbacks and permits

SITE PLAN · 1:200 at A3 · shown in two parts so the narrow 13.5 m plot stays readable

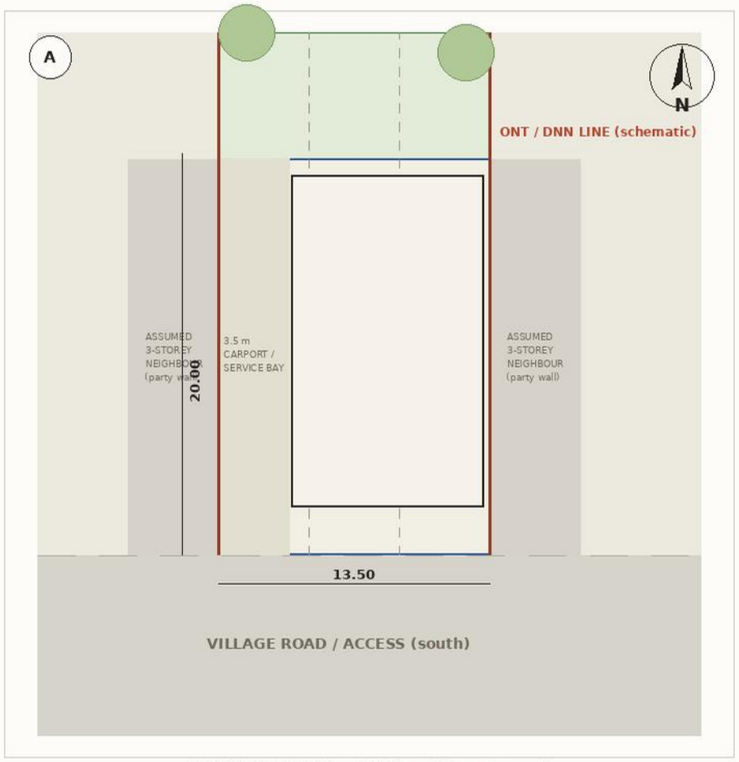

SOUTHERLY PART — ONT band, house, road

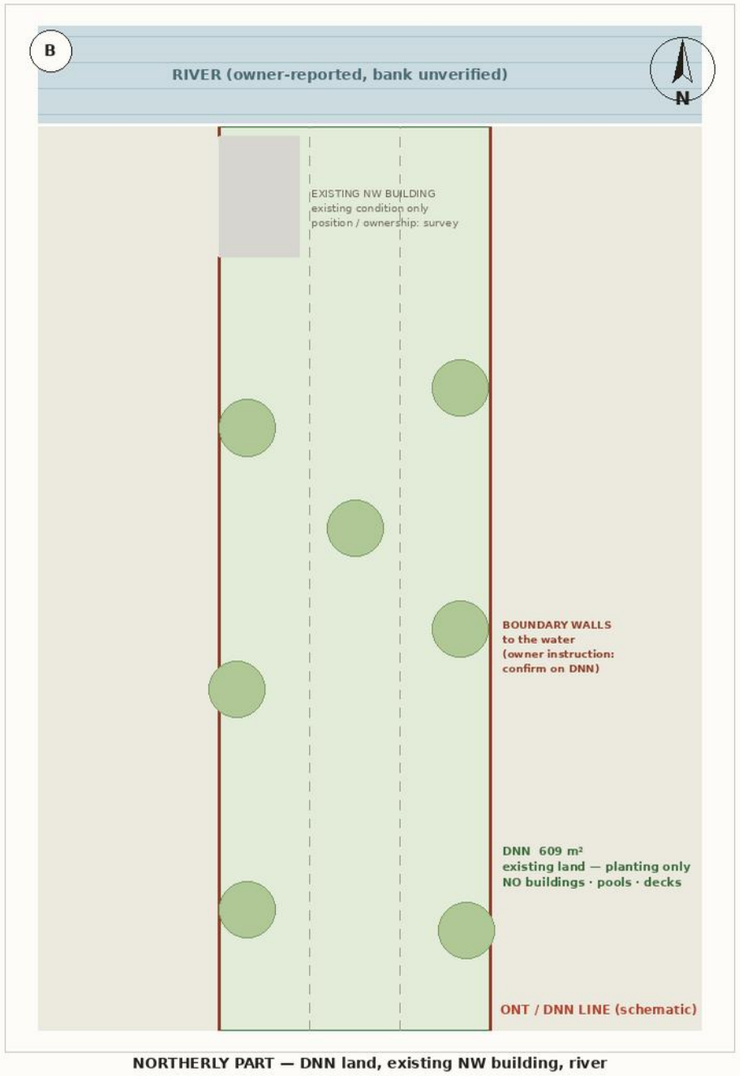

NORTHERLY PART — DNN land, existing NW building, river

NOTES

Schematic site from owner information only: three side-by-side 4.5 m titles, about 13.5 × 65 m. No survey. Corners, levels, bank edge and road reserve are unverified.

Structures are shown ONLY inside the ONT road-side band (3 × 88.8 = 266.4 m²). The 609 m² DNN band is existing land, shown as planting only.

The title sketch shows 6.5 m to the road centreline. It is NOT treated as a verified setback.

Assumed: a 3-storey house on each side built to the property line to about the same 20 m depth. So the east wall is blank (party wall) and the west wall has high-level windows only.

Side boundary walls run the full length to the water on both property lines (owner instruction). This is the only structure on DNN land. Confirm it is permitted.

The existing north-west building is an existing condition only. Its position and ownership are to be surveyed. It is not altered.

Subject to legal merger of the three ONT sections, setbacks, river corridor and permits.

KEY

- ONT — buildable band
- DNN — land / planting only
- service passage
- existing NW building
- assumed 3-storey neighbours
- boundary walls
- house footprint
- assumed / context

0 10 20 30 40 50 metres (assumed — no survey)


CONCEPT 2 — MULTIGENERATIONAL HOUSE

Two storeys · drive-through west carport · central skylight stair + reserved lift · ground-floor suite for the older couple

SCALE	SHEET	STATUS
1:200 at A3	**C2-01** site plan	**FOR REVIEW** *not for construction*


enclosed 158.4 m² · level 1 of 2

GROUND FLOOR · FFL +0.45 / +3.75

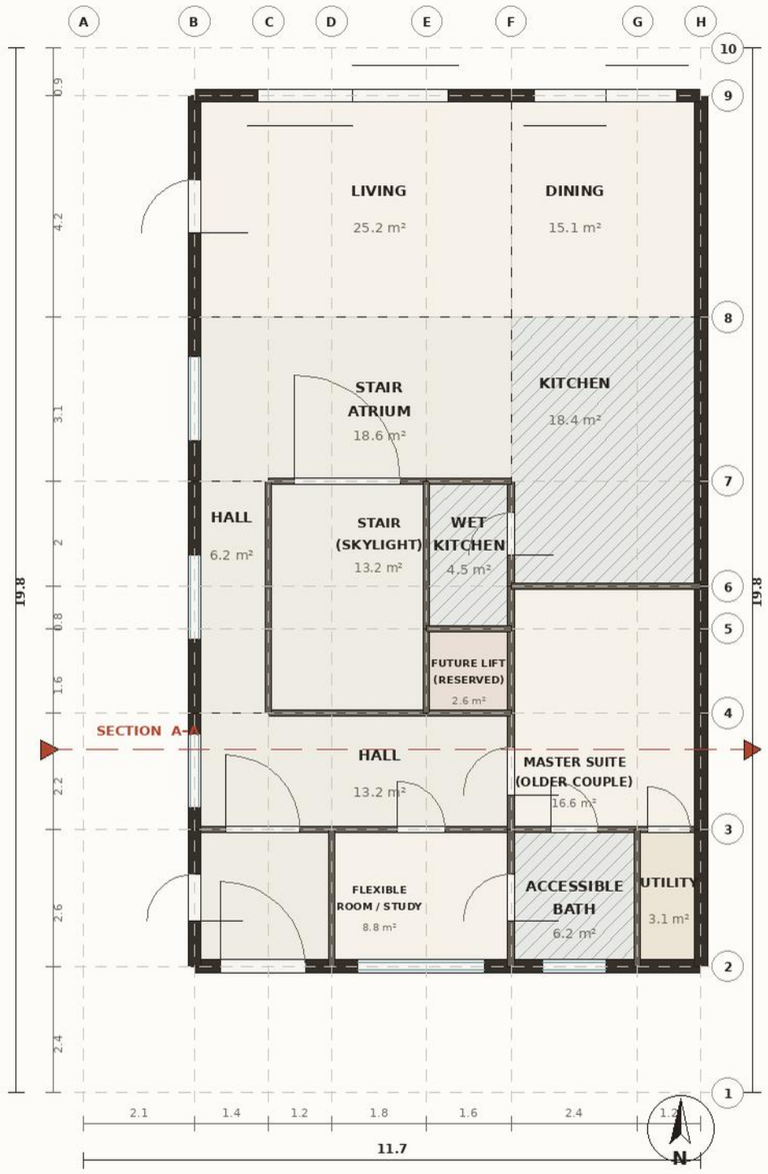

enclosed 137.3 m² · level 2 of 2

UPPER FLOOR · FFL +3.75 / +6.85

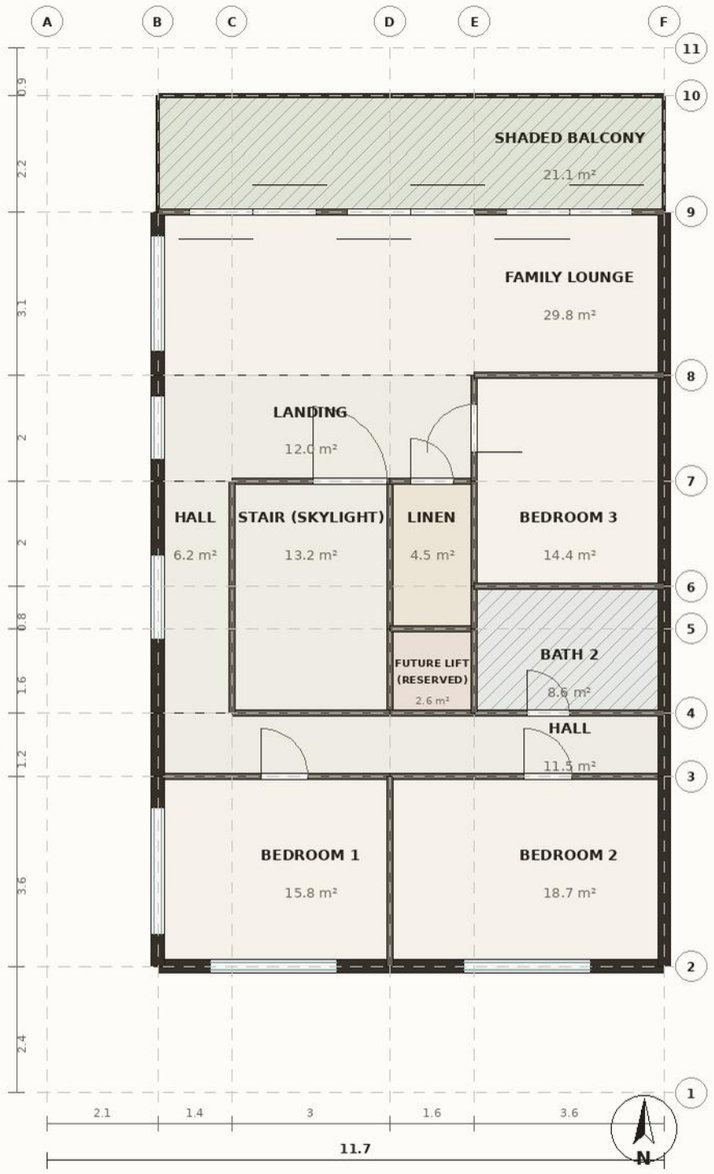

0 10 20 30 40 50 metres (assumed — no survey)

KEY

- HABITABLE
- SERVICE / WET
- CIRCULATION
- STORAGE
- SPECIAL
- OUTDOOR
- PLANT / VOID

NOTES

CONCEPT ONLY — NOT FOR CONSTRUCTION. Dimensions are taken from owner-supplied title information; no survey. Subject to survey, legal merger, setbacks and permits.


Areas are measured from the room rectangles; the balcony and light court are excluded from enclosed area.


CONCEPT 2 — MULTIGENERATIONAL HOUSE

Two storeys · drive-through west carport · central skylight stair + reserved lift · ground-floor suite for the older couple

SCALE	SHEET	STATUS
1:100 at A3	C2-02	FOR REVIEW
	floor plans 1–2	not for construction

ROOF PLAN · looking down

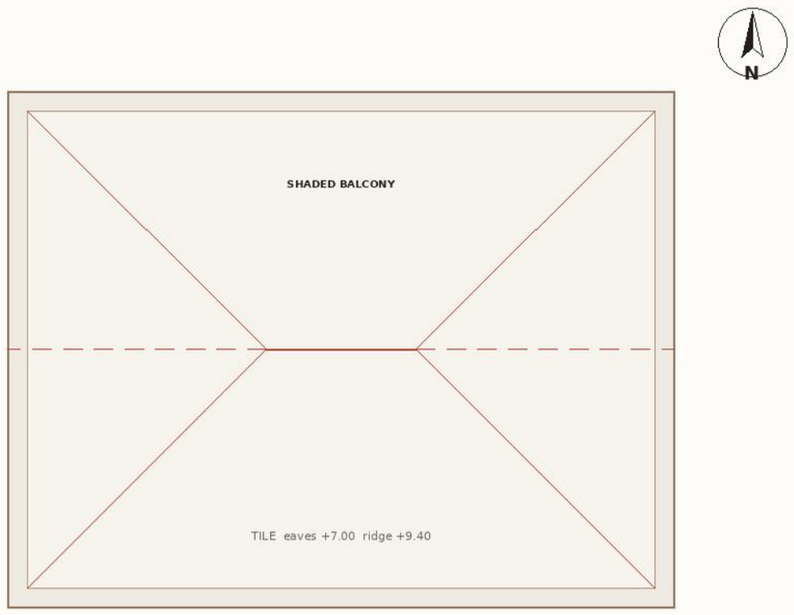

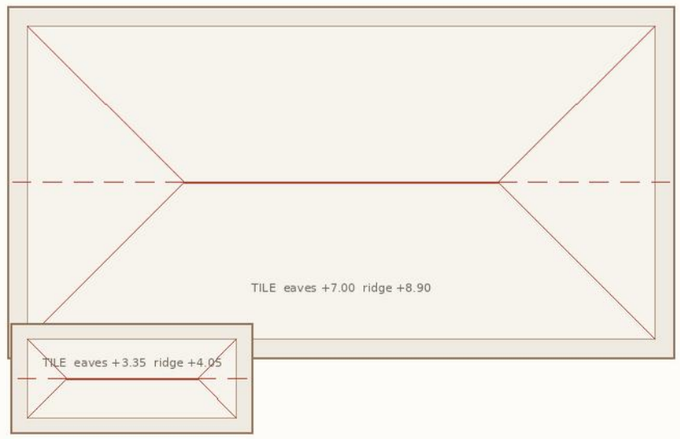

KEY

- roof covering
- ridge / hip
- fascia / eaves
- open slot below

NOTES

ROOF KEY

Ridge and eaves heights come from the option massing: eaves +7.00 m, ridge +9.40 m above datum, 0.30 m overhang all round.

Hips, ridges and the rain-garden slot are derived from the same rectangles as the plans and the 3D model.

Rainwater from the slot and the roof gardens is the only visible drainage; confirm the neighbour-boundary falls before detailing.

- concrete tile on timber — eaves +7.00, ridge +9.40
- ridge / hip line
- fascia / eaves edge, 1.105 m overhang
- rain-garden slot, open to the sky
- outline of the level below (hidden line)


0 10 20 30 40 50 metres (assumed — no survey)

CONCEPT 2 — MULTIGENERATIONAL HOUSE

Two storeys · drive-through west carport · central skylight stair + reserved lift · ground-floor suite for the older couple

SCALE	SHEET	STATUS
1:100 at A3	**C2-03** roof plan	**FOR REVIEW** *not for construction*

SECTION A–A · looking north at y = 6.50 m (assumed cut)

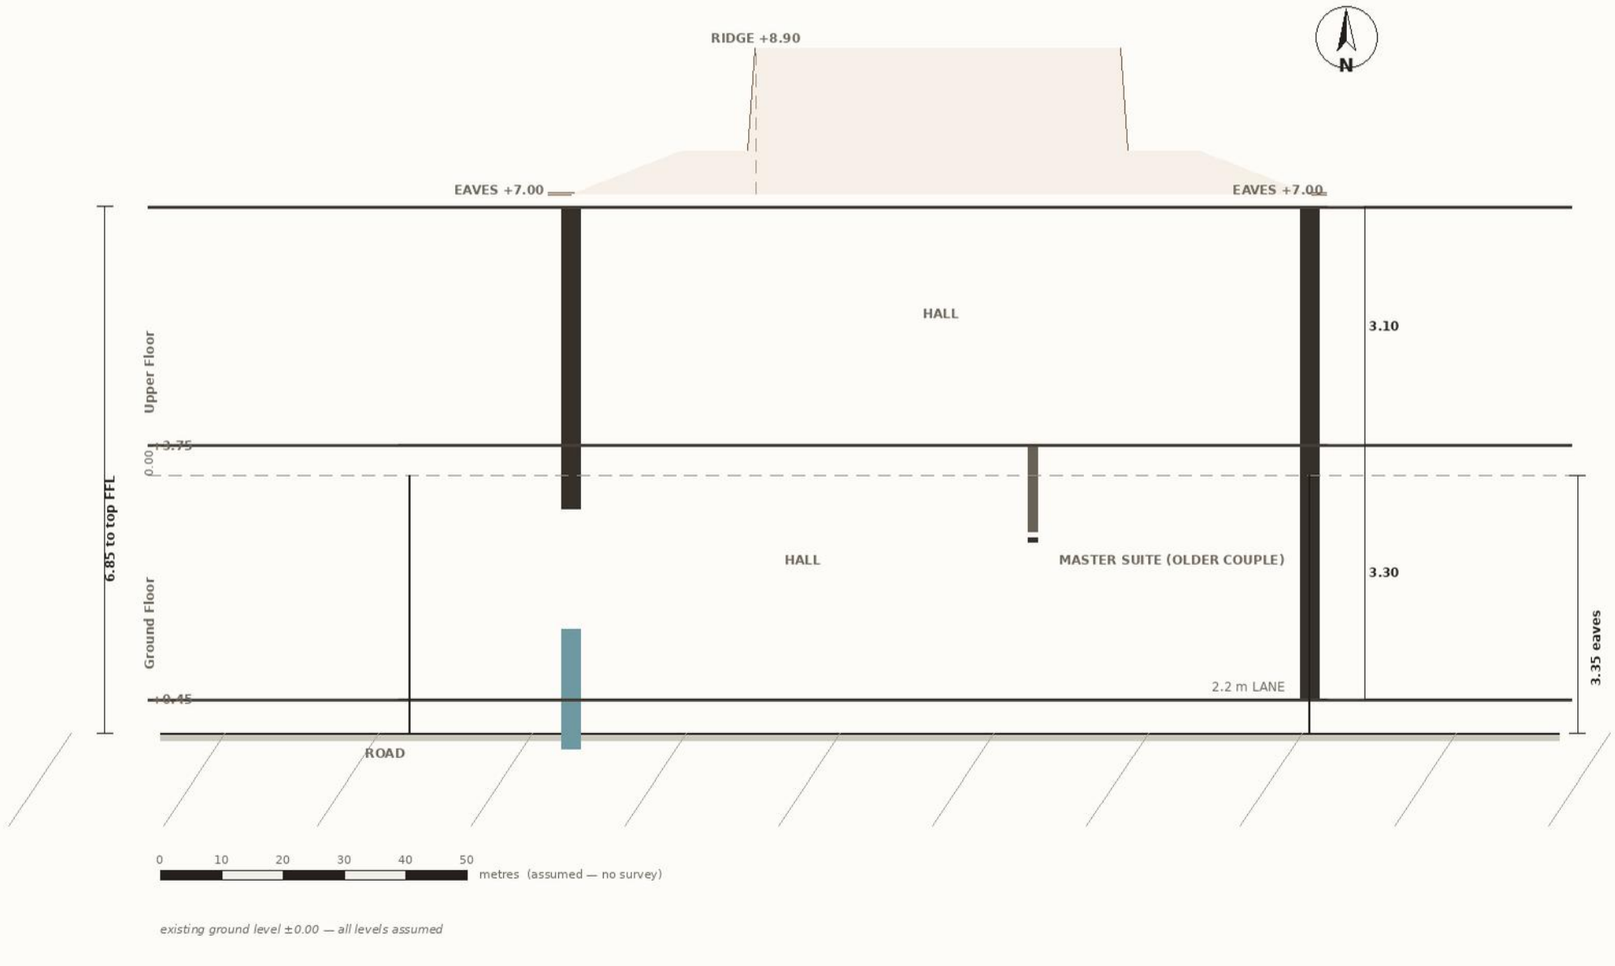

existing ground level ±0.00 — all levels assumed

KEY

- cut external wall, 0.30
- cut internal wall, 0.15
- glazing in the cut
- roof build-up in section

NOTES

Datum 0.00 = existing road and ground level. Finished ground floor +0.45 m, first +3.75 m, eaves +3.35 m, ridge +9.40 m.

Slabs, walls and levels come from the same rectangles as the plans, so the section and the plans can never disagree.

The 2.2 m rain-garden slot is open to the sky on every level: draw it as a full-height void when the structure is detailed.

The cut is at y = 6.50 m. Move it on the plans to suit a later survey.

CONCEPT 2 — MULTIGENERATIONAL HOUSE

Two storeys · drive-through west carport · central skylight stair + reserved lift · ground-floor suite for the older couple

SCALE	SHEET	STATUS
1:100 at A3	**C2-04** section A–A	**FOR REVIEW** *not for construction*

AREA SCHEDULE · net internal, measured from the plan rectangles

Room	Type	Area m²	Cum. m²
Ground Floor · FFL +0.45			
Dining	Habitable	15.1	15.1
Flexible Room / Study	Habitable	8.8	24.0
Living	Habitable	25.2	49.2
Master Suite (older couple)	Habitable	16.6	65.7
Accessible Bath	Service / Wet	6.2	72.0
Stair Atrium	Circulation	18.6	90.6
Entry (Huyền Quan)	Circulation	6.8	97.3
Hall	Circulation	13.2	110.5
Hall	Circulation	6.2	116.7
Kitchen	Service / Wet	18.4	135.0
Future Lift (reserved)	Special	2.6	137.6
Stair (skylight)	Circulation	13.2	150.8
Utility	Storage	3.1	153.9
Wet Kitchen	Service / Wet	4.5	158.4
Level total, enclosed		**158.4**	
Upper Floor · FFL +3.75			
Bedroom 1	Habitable	15.8	15.8
Bedroom 2	Habitable	18.7	34.6
Bedroom 3	Habitable	14.4	49.0
Family Lounge	Habitable	29.8	78.7
Shaded Balcony	Outdoor	21.1	99.8
Bath 2	Service / Wet	8.6	108.5
Hall	Circulation	11.5	120.0
Hall	Circulation	6.2	126.2
Landing	Circulation	12.0	138.2
Future Lift (reserved)	Special	2.6	140.7
Linen	Storage	4.5	145.2
Stair (skylight)	Circulation	13.2	158.4
Level total, enclosed		**137.3**	

AREA SUMMARY	Area
Level 1 — Ground Floor (enclosed)	158.4 m²
Level 2 — Upper Floor (enclosed)	137.3 m²
Total enclosed floor area	**295.7 m²**

ORDER OF COST — TURNKEY, NORTHERN VIET NAM

INDICATIVE BUILD COST	M VND	+10% prov.
Basic build — 4.9 M VND/m²	1 449	1 594
Mid build — 6.5 M VND/m²	1 922	2 114
High build — 8.5 M VND/m²	2 513	2 765

NOTES

Areas are net internal floor areas computed from the room rectangles. Terraces, loggias, the rain-garden slot, the plant deck and roof gardens are excluded from the totals but shown on the plans.

The build-cost range is a rule of thumb from published Vietnamese cost guides for northern Viet Nam, not a quotation. It excludes site works, boundary treatment and furniture.

Confirm with a local quantity surveyor and at least two builders before committing to a budget.

NOTES

No habitable room here is below 2.7 m clear. The ground floor is a complete one-level home — bedroom, bathroom, living, dining and kitchen all at +0.45 — so the family can live on one level for as long as they want to.

Order-of-cost at 4.9–8.5 M VND/m² turnkey (northern Viet Nam) is in the table on the left. It is a rule of thumb, not a quotation.

ROOM TYPE KEY

- HABITABLE
- SERVICE / WET
- CIRCULATION
- STORAGE
- SPECIAL
- OUTDOOR
- PLANT / VOID

CONCEPT 2 — MULTIGENERATIONAL HOUSE

Two storeys · drive-through west carport · central skylight stair + reserved lift · ground-floor suite for the older couple

SCALE	SHEET	STATUS
as noted	**C2-05** area schedule	**FOR REVIEW** *not for construction*

Blender views

Cycles renders from the same data as the drawings and the walkthrough



Street view



From the river end, between the boundary walls

CONCEPT ONLY — NOT FOR CONSTRUCTION · subject to survey, legal merger, setbacks and permits

Blender views

Cycles renders from the same data as the drawings and the walkthrough



Drive-through carport / service bay



Aerial


CONCEPT ONLY — NOT FOR CONSTRUCTION · subject to survey, legal merger, setbacks and permits

Blender views

Cycles renders from the same data as the drawings and the walkthrough



Upper balcony looking north

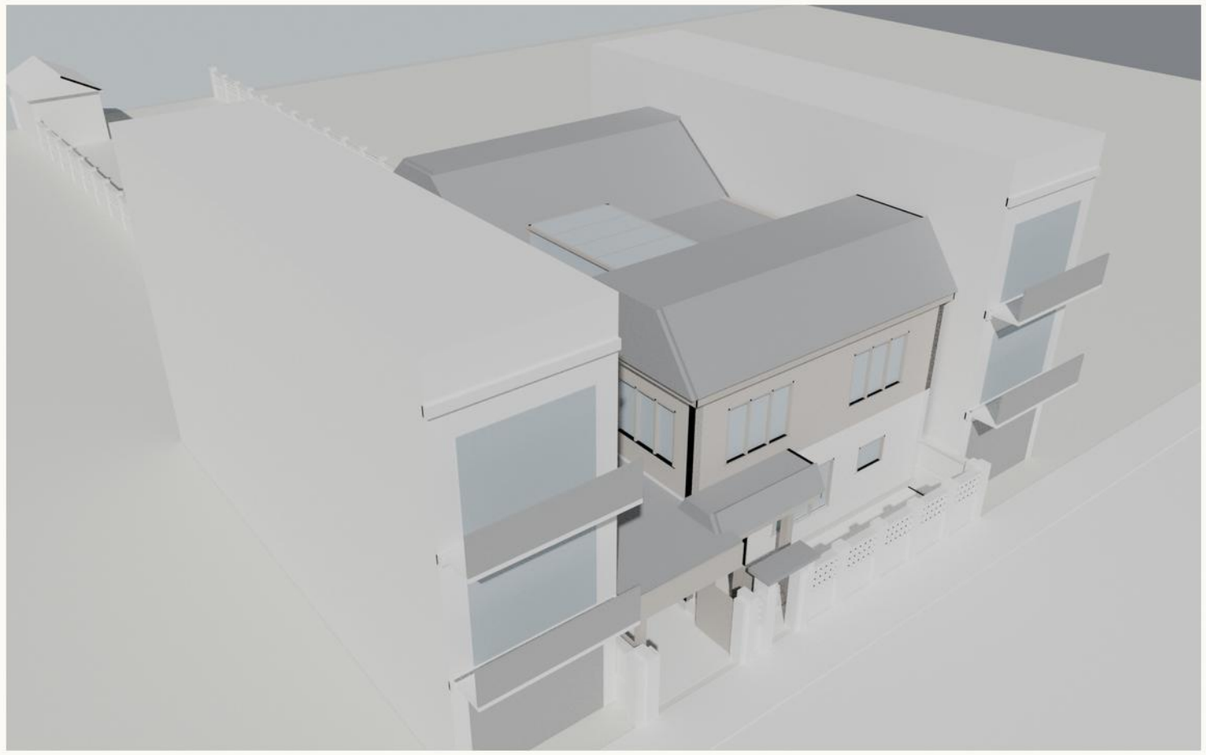

Clay massing

CONCEPT ONLY — NOT FOR CONSTRUCTION · subject to survey, legal merger, setbacks and permits

Walkthrough (Unity)


Interactive model: these are fixed viewpoints you can jump to with keys 1–9




Street



Carport

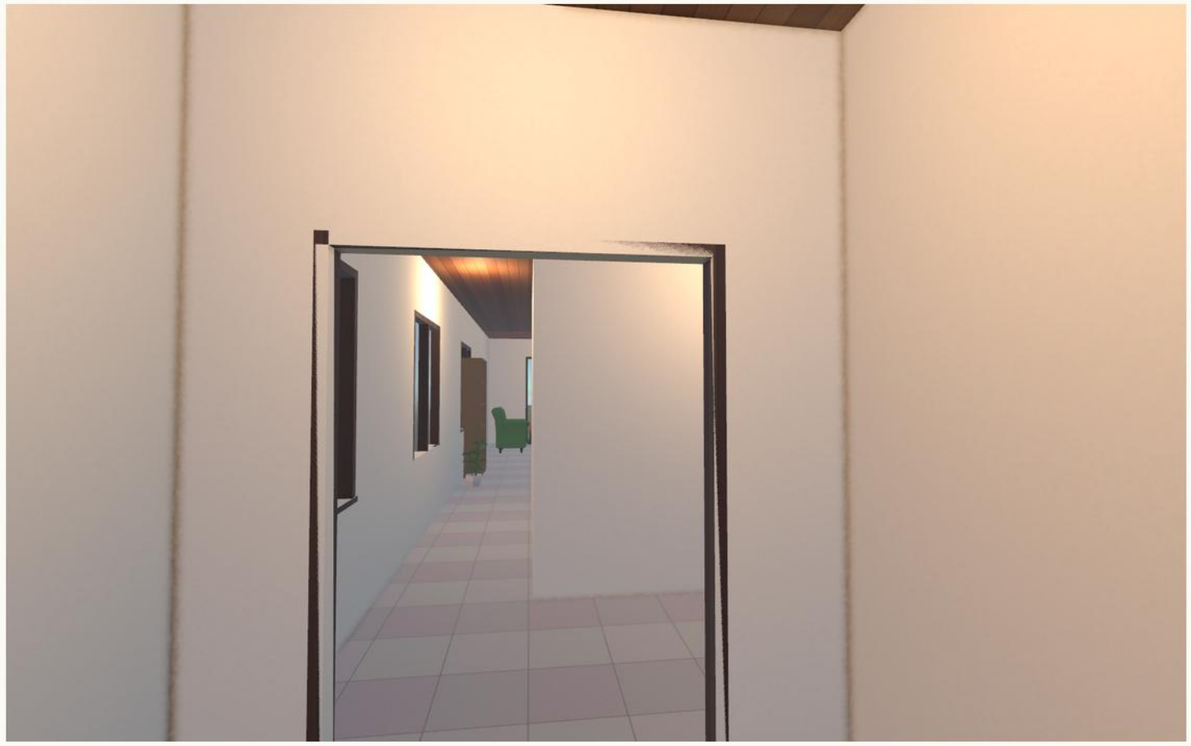

Entry

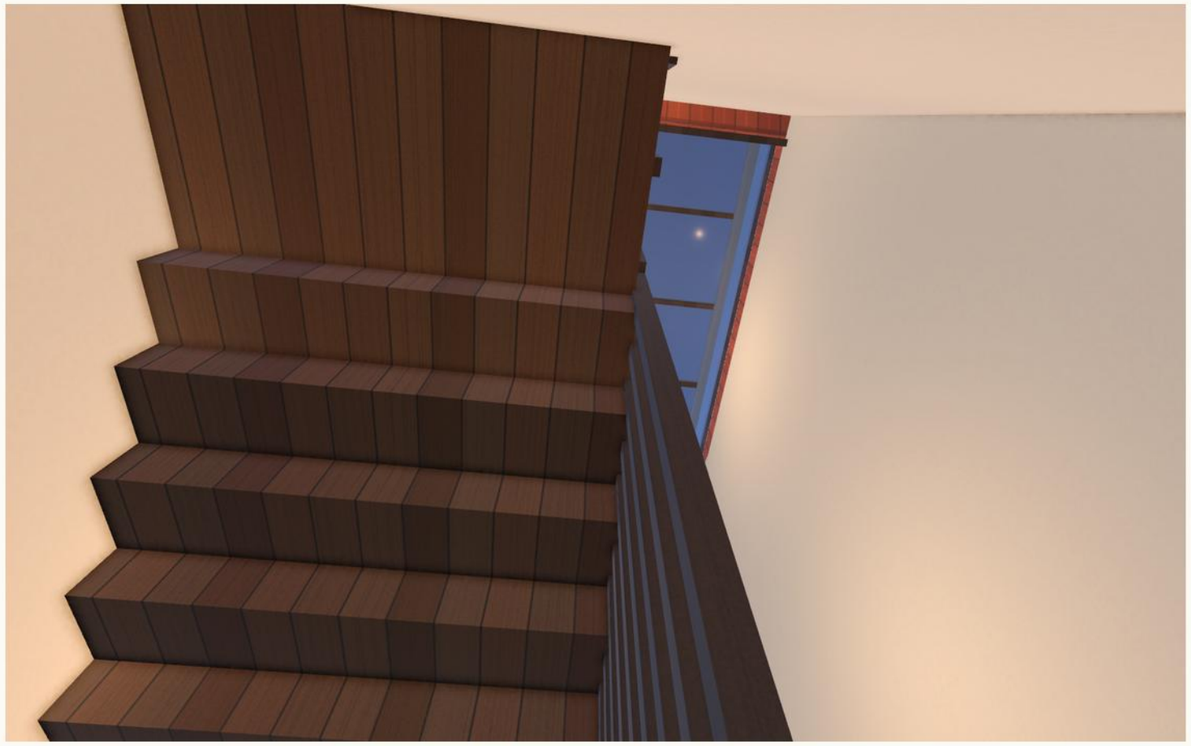

Atrium

CONCEPT ONLY — NOT FOR CONSTRUCTION · subject to survey, legal merger, setbacks and permits

Walkthrough (Unity)

Interactive model: these are fixed viewpoints you can jump to with keys 1–9




Living



Master



Lounge

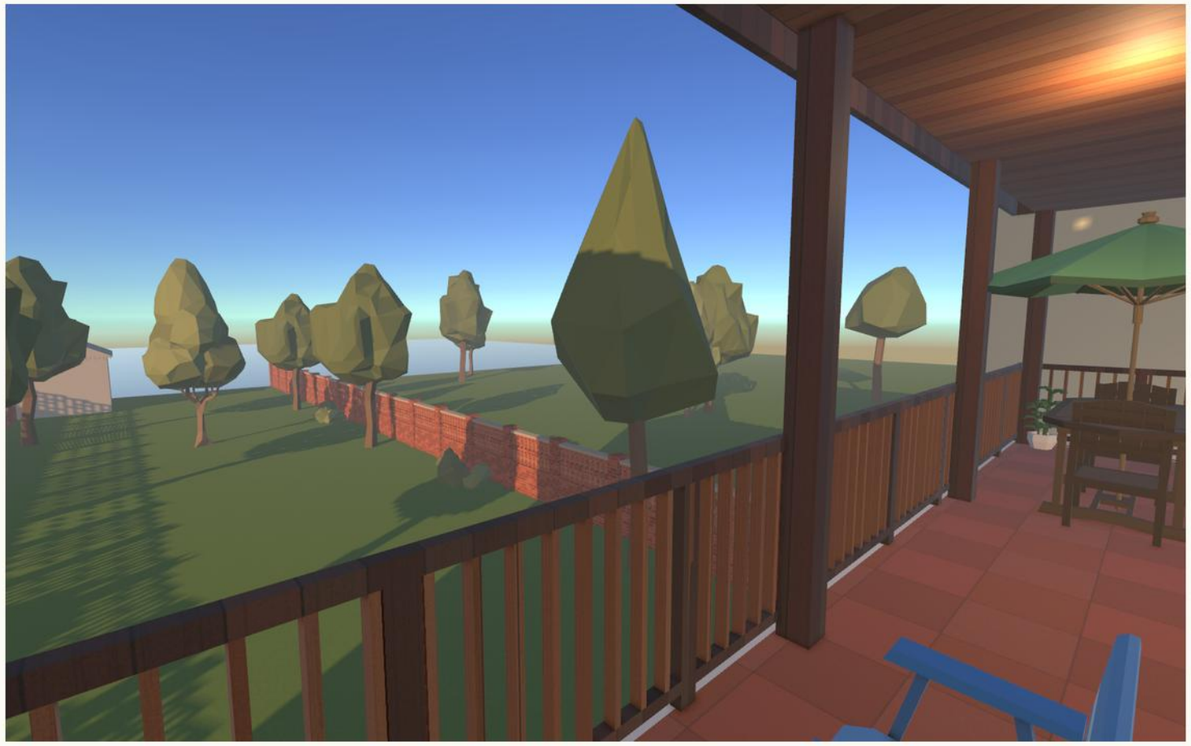


Balcony


CONCEPT ONLY — NOT FOR CONSTRUCTION · subject to survey, legal merger, setbacks and permits

Walkthrough (Unity)


Interactive model: these are fixed viewpoints you can jump to with keys 1–9

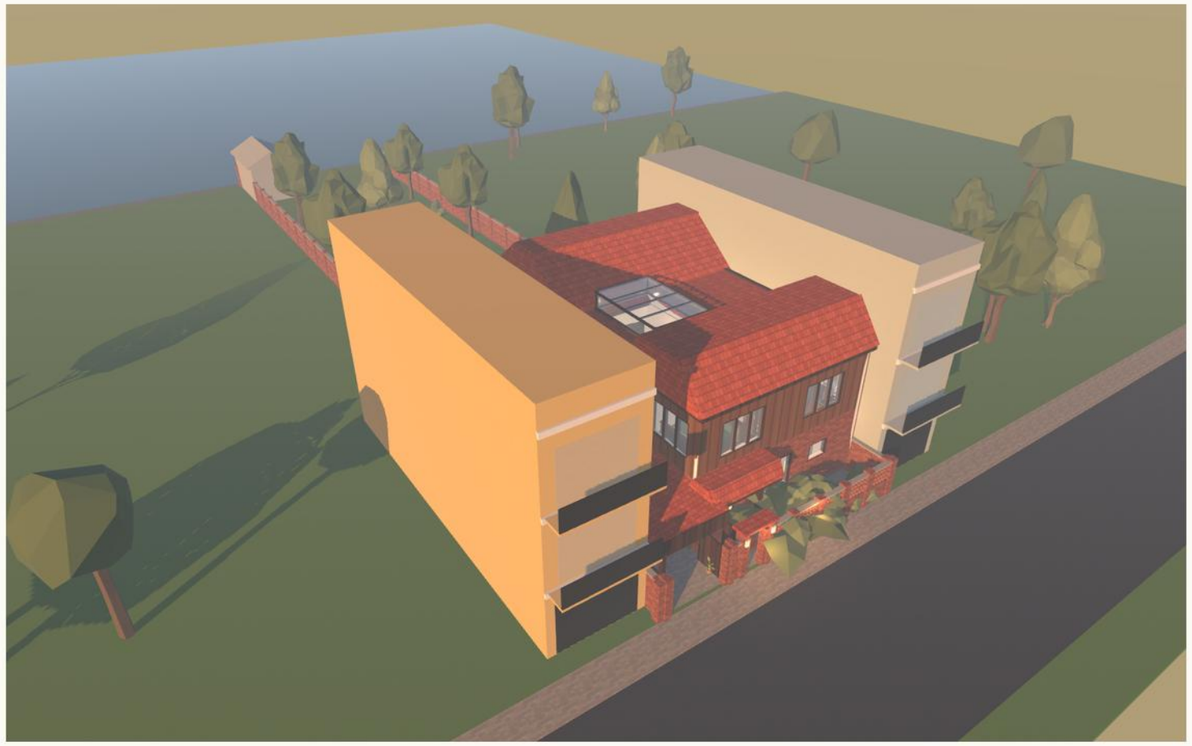

Aerial

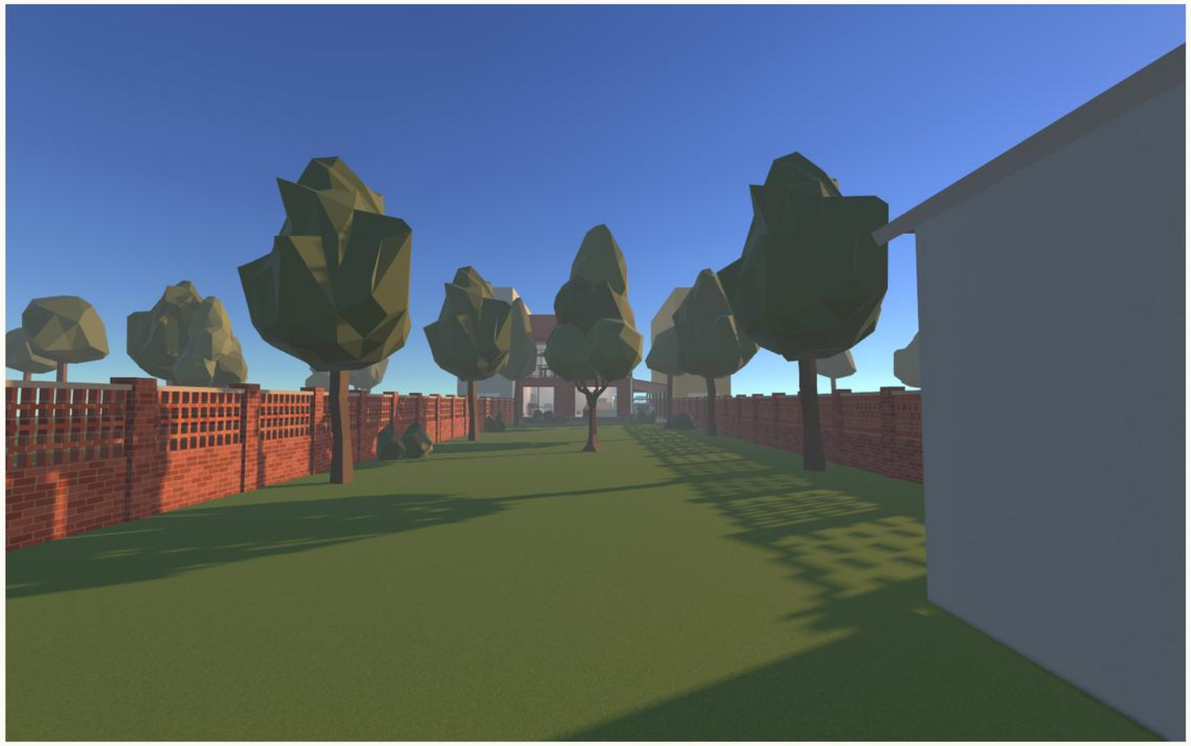

Riverside

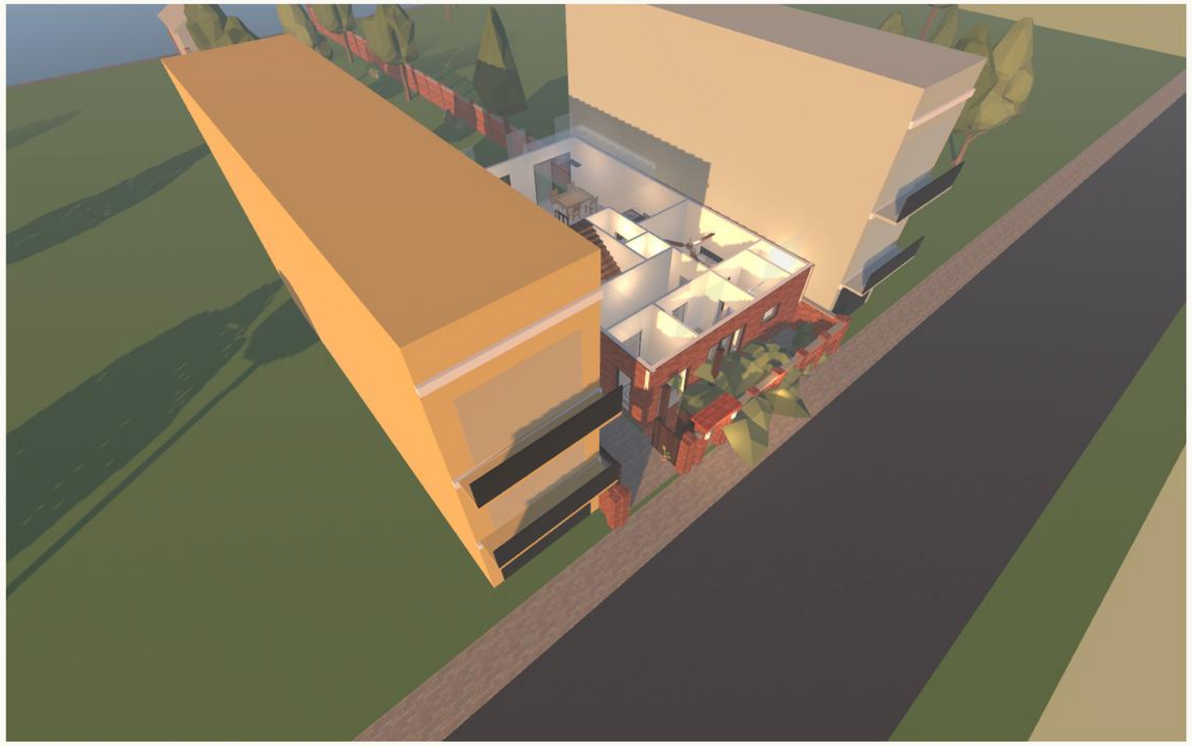

Dollhouse Ground

CONCEPT ONLY — NOT FOR CONSTRUCTION · subject to survey, legal merger, setbacks and permits