CONCEPT 3 — FOUR-BED GARAGE HOUSE

Two storeys · double garage · home office · open kitchen, meals and family to a rear alfresco · four bedrooms + rumpus



Blender render — street view (golden hour)



Blender render — aerial from the south-west

A compact, modern two-storey house with flat roofs behind parapets. The walls are white render downstairs and white vertical cladding upstairs, with a stone pier at the entry and a dark panel garage door. A double garage sits against the blank east party wall. The front door opens to a foyer with the home office beside it and a U-shaped stair behind. A hallway passes the powder room and laundry to the open-plan kitchen, meals and family room across the back, which opens to a covered alfresco facing the river garden. A butler's pantry links the kitchen and the garage. Upstairs, a rumpus room faces the street. The rear bedroom suite has a double walk-in robe and ensuite, and there are three more bedrooms, a bathroom, a powder room and a linen walk-in. A covered deck off Bedroom 4 sits on the garage roof. A 2.8 m garden strip runs down the west side. The DNN land holds only the boundary walls and planting.

THE CONCEPT IN NUMBERS


Footprint	137.3 m² (52% of ONT band)
Ground floor	121 m² enclosed
Upper floor	117 m² enclosed + 7 m² balcony
Total enclosed	238 m²
Constraint check	PASS — all structures in ONT; DNN planting only

Walkthrough test: 32/32 rooms reachable


The house is fitted to the 13.5 m frontage at its brochure width of 10.4 m. That leaves a 2.8 m garden strip on the west, and the garage sits 0.3 m off the east party wall. The rear wall is at y 16.2 m, so the alfresco (4.3 × 2.8 m) stays inside the ONT band, ending at 19.0 m against the 19.73 m limit. Nothing is built on the DNN land except the boundary walls. The garage door is set 3.9 m behind the 2.0 m front wall, which is enough for the gate leaves and a short apron, but not to park in front of the garage. The plan is adapted from a commercial volume-builder design for study only. Building it would need the design owner's licence or a new design.

CONCEPT ONLY — NOT FOR CONSTRUCTION · subject to survey, legal merger, setbacks and permits

SITE PLAN · 1:200 at A3 · shown in two parts so the narrow 13.5 m plot stays readable

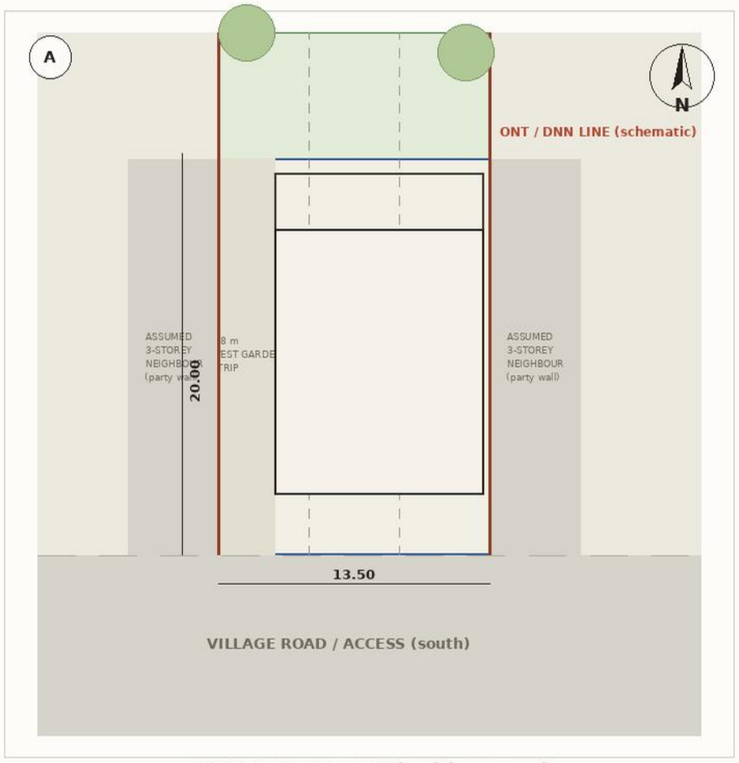

SOUTHERLY PART — ONT band, house, road

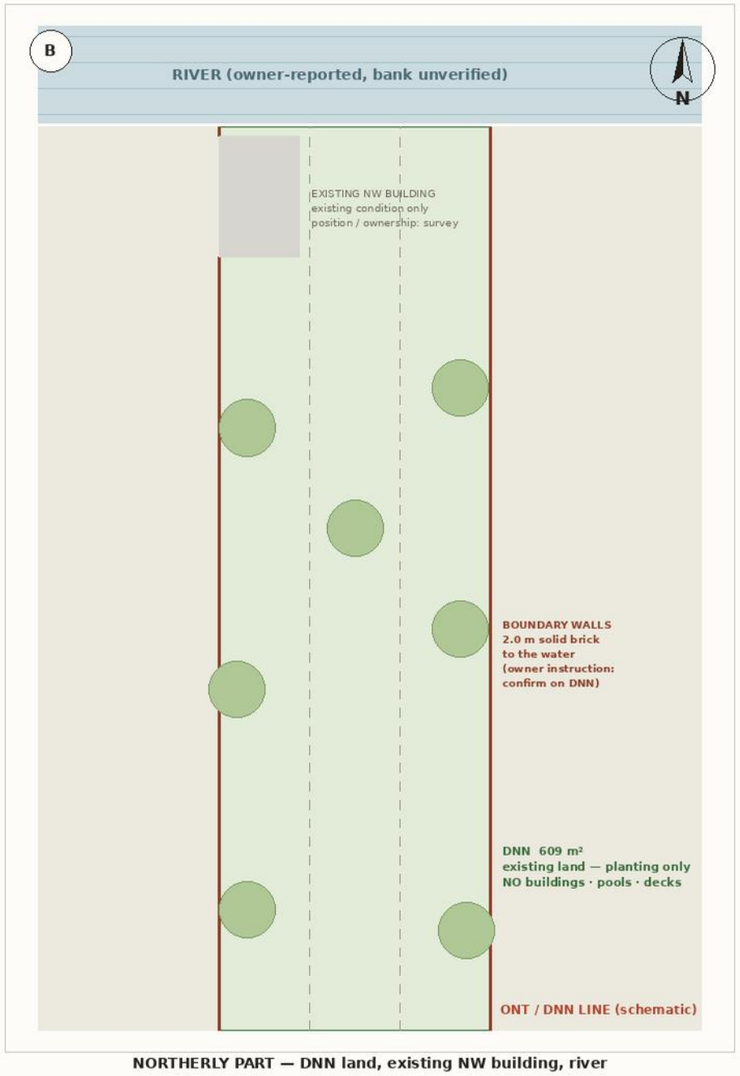

NORTHERLY PART — DNN land, existing NW building, river

NOTES

Schematic site from owner information only: three side-by-side 4.5 m titles, about 13.5 × 65 m. No survey. Corners, levels, bank edge and road reserve are unverified.

Structures are shown ONLY inside the ONT road-side band (3 × 88.8 = 266.4 m²). The 609 m² DNN band is existing land, shown as planting only.

The title sketch shows 6.5 m to the road centreline. It is NOT treated as a verified setback.

Assumed: a 3-storey house on each side built to the property line to about the same 20 m depth. So the east wall is blank (party wall) and the west wall has high-level windows only.

Side boundary walls run the full length to the water on both property lines (owner instruction). This is the only structure on DNN land. Confirm it is permitted.

The existing north-west building is an existing condition only. Its position and ownership are to be surveyed. It is not altered.

Subject to legal merger of the three ONT sections, setbacks, river corridor and permits.

KEY

- ONT — buildable band
- DNN — land / planting only
- service passage
- existing NW building
- assumed 3-storey neighbours
- boundary walls
- house footprint
- assumed / context

0 10 20 30 40 50 metres (assumed — no survey)


CONCEPT 3 — FOUR-BED GARAGE HOUSE

Two storeys · double garage · home office · open kitchen, meals and family to a rear alfresco · four bedrooms + rumpus

SCALE	SHEET	STATUS
1:200 at A3	**C3-01** site plan	**FOR REVIEW** *not for construction*


enclosed 123.3 m² · level 1 of 2

GROUND FLOOR · FFL +0.15 / +3.15

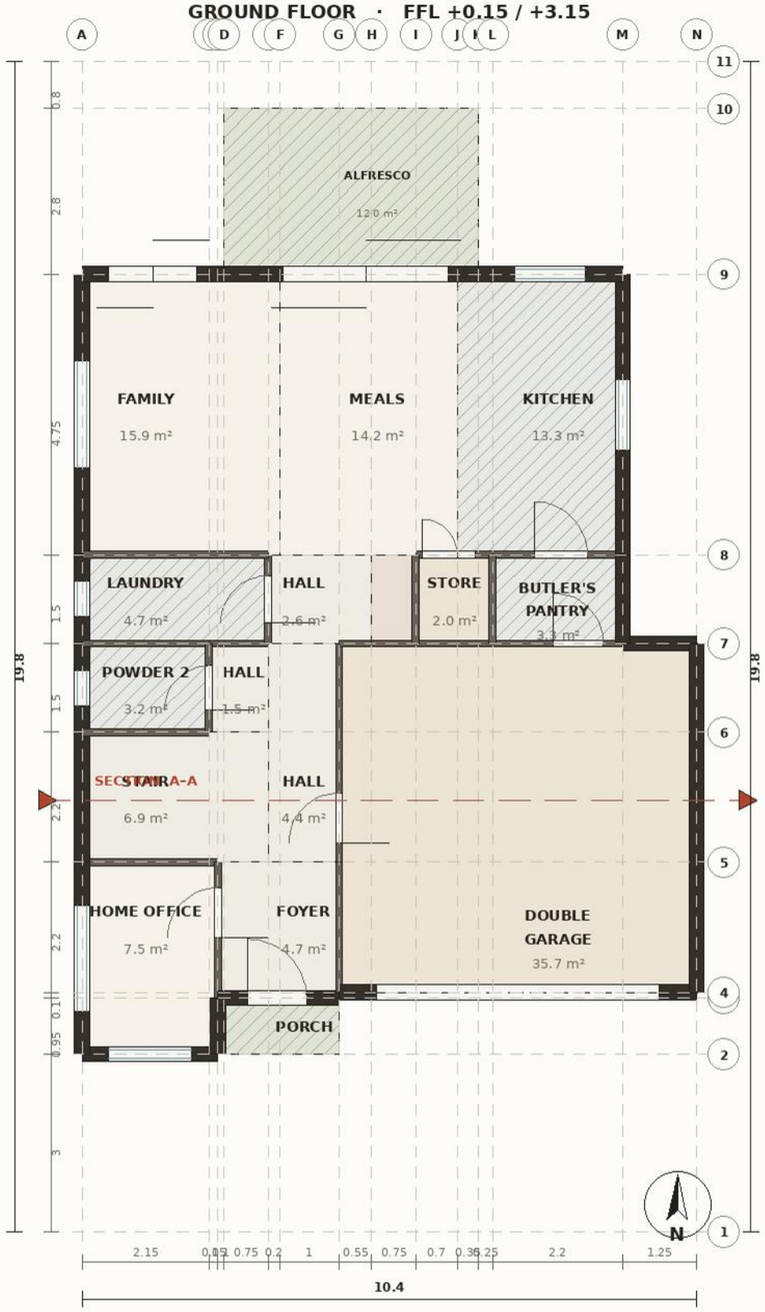

enclosed 129.9 m² · level 2 of 2

UPPER FLOOR · FFL +3.15 / +5.85

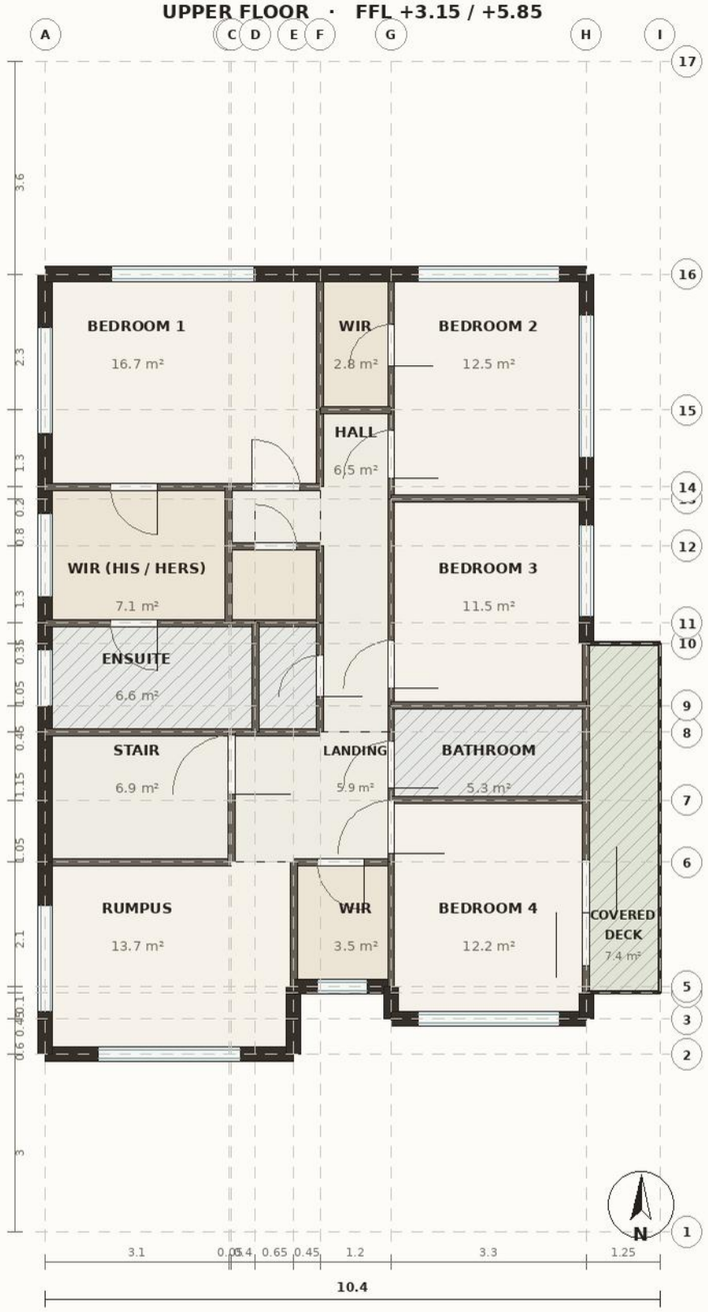

0 10 20 30 40 50 metres (assumed — no survey)

KEY

- HABITABLE
- SERVICE / WET
- CIRCULATION
- STORAGE
- SPECIAL
- OUTDOOR
- PLANT / VOID

NOTES

CONCEPT ONLY — NOT FOR CONSTRUCTION. Dimensions are taken from owner-supplied title information; no survey. Subject to survey, legal merger, setbacks and permits.


Areas are measured from the room rectangles; the balcony and light court are excluded from enclosed area.

CONCEPT 3 — FOUR-BED GARAGE HOUSE

Two storeys · double garage · home office · open kitchen, meals and family to a rear alfresco · four bedrooms + rumpus

SCALE	SHEET	STATUS
1:100 at A3	C3-02	FOR REVIEW
	floor plans 1–2	*not for construction*

ROOF PLAN · looking down

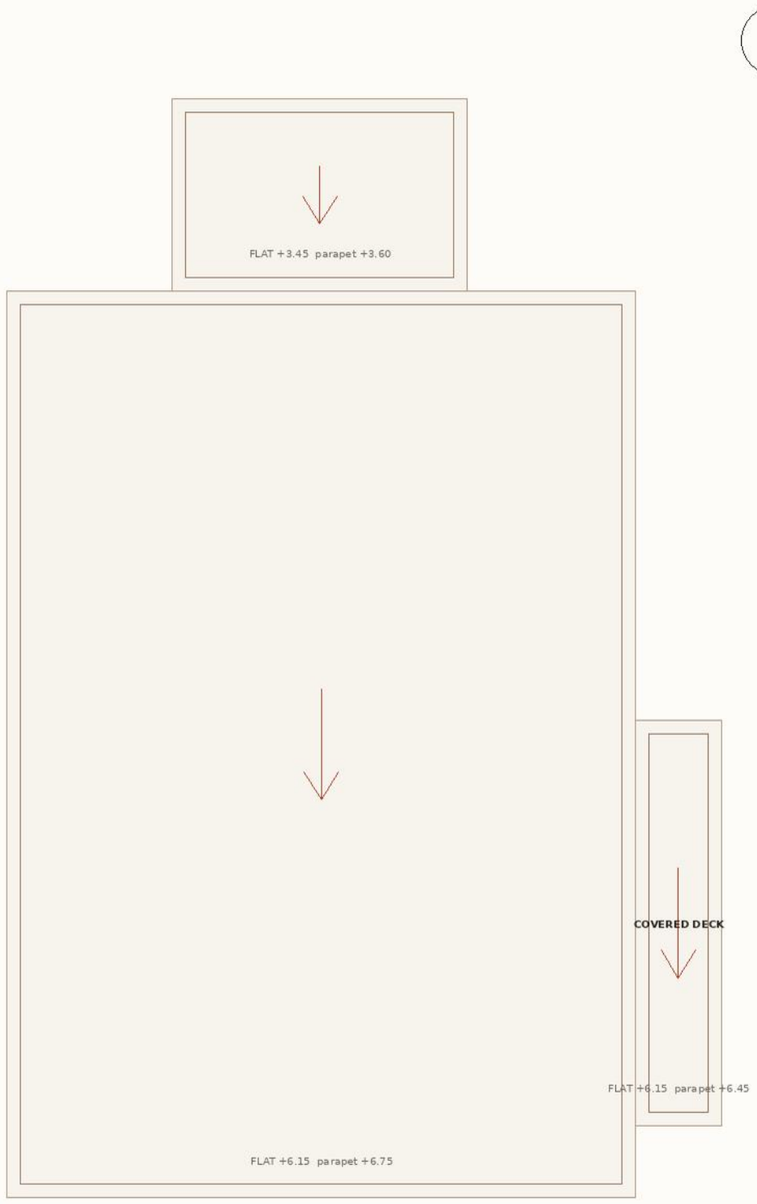

0 10 20 30 40 50 metres (assumed — no survey)

KEY

- roof covering
- fall arrow
- parapet
- open slot below

ROOF KEY

- membrane flat roofs behind parapets — deck +6.15, parapet +6.75
- fall arrow (to box gutter / outlet)
- parapet inner line
- outline of the level below (hidden line)

NOTES


Flat roofs: membrane deck +6.15 m, parapets up to +6.75 m above datum, no overhang. Falls and outlets to be set at design development.
Roof outlines come from the same rectangles as the plans and the 3D model.
Rainwater: box gutters behind the parapets to downpipes inside the site; nothing may discharge onto the neighbours.

CONCEPT 3 — FOUR-BED GARAGE HOUSE

Two storeys · double garage · home office · open kitchen, meals and family to a rear alfresco · four bedrooms + rumpus

SCALE	SHEET	STATUS
1:100 at A3	**C3-03** roof plan	**FOR REVIEW** *not for construction*

SECTION A–A · looking north at y = 7.30 m (assumed cut)

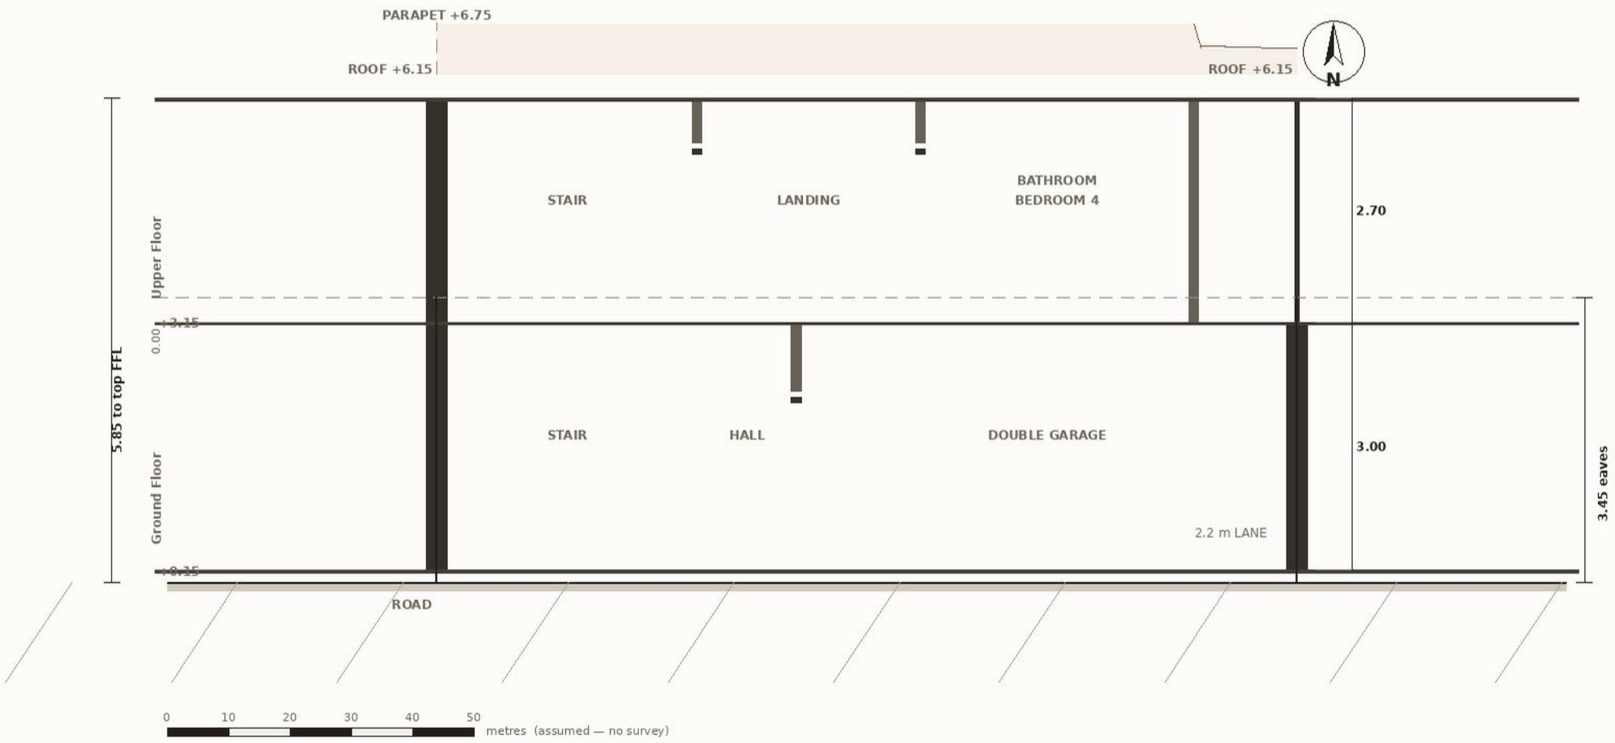

existing ground level ±0.00 — all levels assumed

KEY

- cut external wall, 0.30
- cut internal wall, 0.15
- glazing in the cut
- roof build-up in section

NOTES

Datum 0.00 = existing road and ground level. Finished ground floor +0.15 m, first +3.15 m, eaves +3.45 m, ridge +6.75 m.

Slabs, walls and levels come from the same rectangles as the plans, so the section and the plans can never disagree.

The 2.2 m rain-garden slot is open to the sky on every level: draw it as a full-height void when the structure is detailed.

The cut is at y = 7.30 m. Move it on the plans to suit a later survey.

CONCEPT 3 — FOUR-BED GARAGE HOUSE

Two storeys · double garage · home office · open kitchen, meals and family to a rear alfresco · four bedrooms + rumpus

SCALE	SHEET	STATUS
1:100 at A3	**C3-04** section A–A	**FOR REVIEW** *not for construction*

AREA SCHEDULE · net internal, measured from the plan rectangles

Room	Type	Area m²	Cum. m²
Ground Floor · FFL +0.15			
Family	Habitable	15.9	15.9
Meals	Habitable	14.2	30.2
Home Office	Habitable	7.5	37.6
Alfresco	Outdoor	12.0	49.7
Foyer	Circulation	4.7	54.4
Double Garage	Storage	35.7	90.1
Hall	Circulation	4.4	94.5
Hall	Circulation	2.6	97.2
Hall	Circulation	1.5	98.7
IT Nook	Special	1.1	99.8
Kitchen	Service / Wet	13.3	113.1
Laundry	Service / Wet	4.7	117.8
Butler's Pantry	Service / Wet	3.3	121.1
Porch	Outdoor	1.9	123.0
Powder 2	Service / Wet	3.2	126.3
Stair	Circulation	6.9	133.2
Store	Storage	2.0	135.2
Level total, enclosed		**123.3**	
Upper Floor · FFL +3.15			
Bedroom 1	Habitable	16.7	16.7
Bedroom 2	Habitable	12.5	29.3
Bedroom 3	Habitable	11.5	40.8
Bedroom 4	Habitable	12.2	53.0
Rumpus	Habitable	13.7	66.7
Bathroom	Service / Wet	5.3	72.0
Covered Deck	Outdoor	7.4	79.3
Ensuite	Service / Wet	6.6	85.9
Hall	Circulation	6.5	92.5
Hall	Circulation	1.5	94.0
Landing	Circulation	5.9	99.9
Powder 1	Service / Wet	2.0	102.0
Stair	Circulation	6.9	108.9
Linen	Storage	2.0	110.9
WIR (his / hers)	Storage	7.1	118.1
WIR	Storage	2.8	120.8
WIR	Storage	3.5	124.3
Level total, enclosed		**129.9**	

AREA SUMMARY	Area
Level 1 — Ground Floor (enclosed)	123.3 m²
Level 2 — Upper Floor (enclosed)	129.9 m²
Total enclosed floor area	**253.2 m²**

ORDER OF COST — TURNKEY, NORTHERN VIET NAM

INDICATIVE BUILD COST	M VND	+10% prov.
Basic build — 4.9 M VND/m²	1 241	1 365
Mid build — 6.5 M VND/m²	1 646	1 810
High build — 8.5 M VND/m²	2 152	2 367

NOTES

Areas are net internal floor areas computed from the room rectangles. Terraces, loggias, the rain-garden slot, the plant deck and roof gardens are excluded from the totals but shown on the plans.

The build-cost range is a rule of thumb from published Vietnamese cost guides for northern Viet Nam, not a quotation. It excludes site works, boundary treatment and furniture.

Confirm with a local quantity surveyor and at least two builders before committing to a budget.

NOTES

No habitable room here is below 2.7 m clear. The ground floor is a complete one-level home — bedroom, bathroom, living, dining and kitchen all at +0.15 — so the family can live on one level for as long as they want to.

Order-of-cost at 4.9–8.5 M VND/m² turnkey (northern Viet Nam) is in the table on the left. It is a rule of thumb, not a quotation.

ROOM TYPE KEY

- HABITABLE
- SERVICE / WET
- CIRCULATION
- STORAGE
- SPECIAL
- OUTDOOR
- PLANT / VOID

CONCEPT 3 — FOUR-BED GARAGE HOUSE

Two storeys · double garage · home office · open kitchen, meals and family to a rear alfresco · four bedrooms + rumpus

SCALE	SHEET	STATUS
as noted	**C3-05** area schedule	**FOR REVIEW** *not for construction*

Blender views

Cycles renders from the same data as the drawings and the walkthrough



Street view



From the garden (DNN land, planting only)

CONCEPT ONLY — NOT FOR CONSTRUCTION · subject to survey, legal merger, setbacks and permits

Blender views

Cycles renders from the same data as the drawings and the walkthrough



From the river end, between the boundary walls



Foyer looking down the hall to the living area

CONCEPT ONLY — NOT FOR CONSTRUCTION · subject to survey, legal merger, setbacks and permits

Blender views

Cycles renders from the same data as the drawings and the walkthrough



Family, meals and kitchen opening to the alfresco




Aerial


CONCEPT ONLY — NOT FOR CONSTRUCTION · subject to survey, legal merger, setbacks and permits

Blender views

Cycles renders from the same data as the drawings and the walkthrough

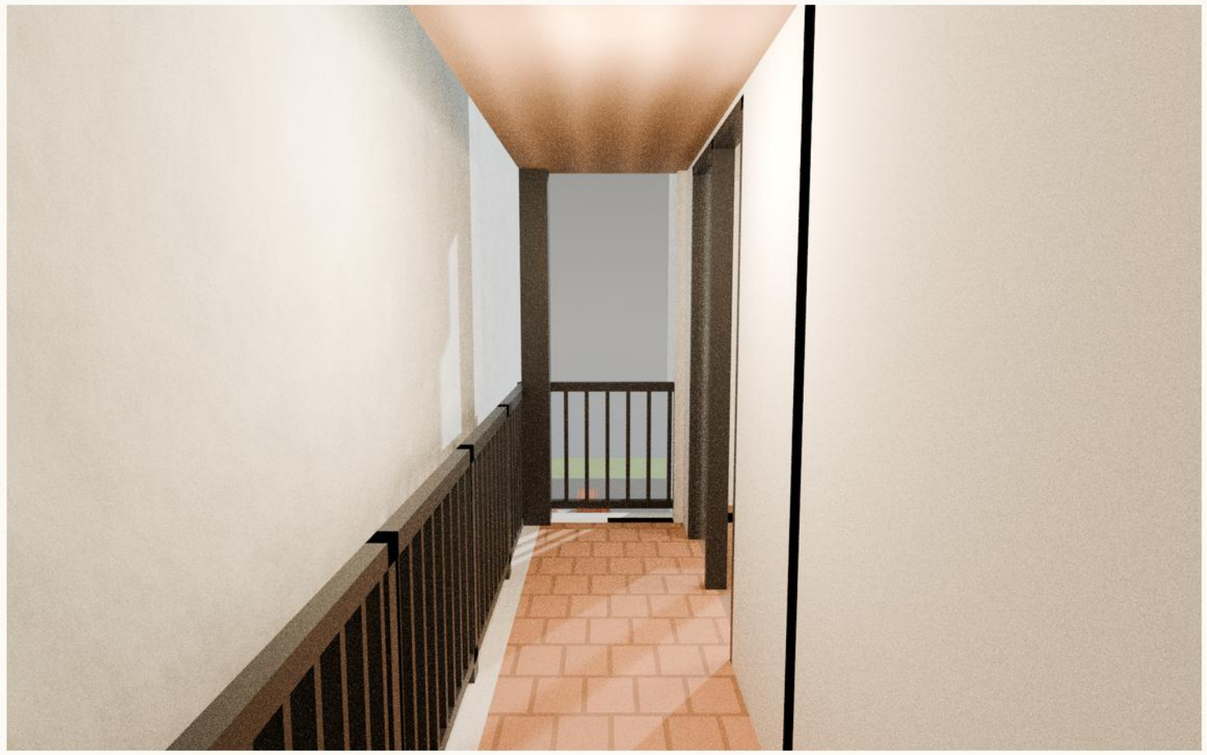

Covered deck on the garage roof

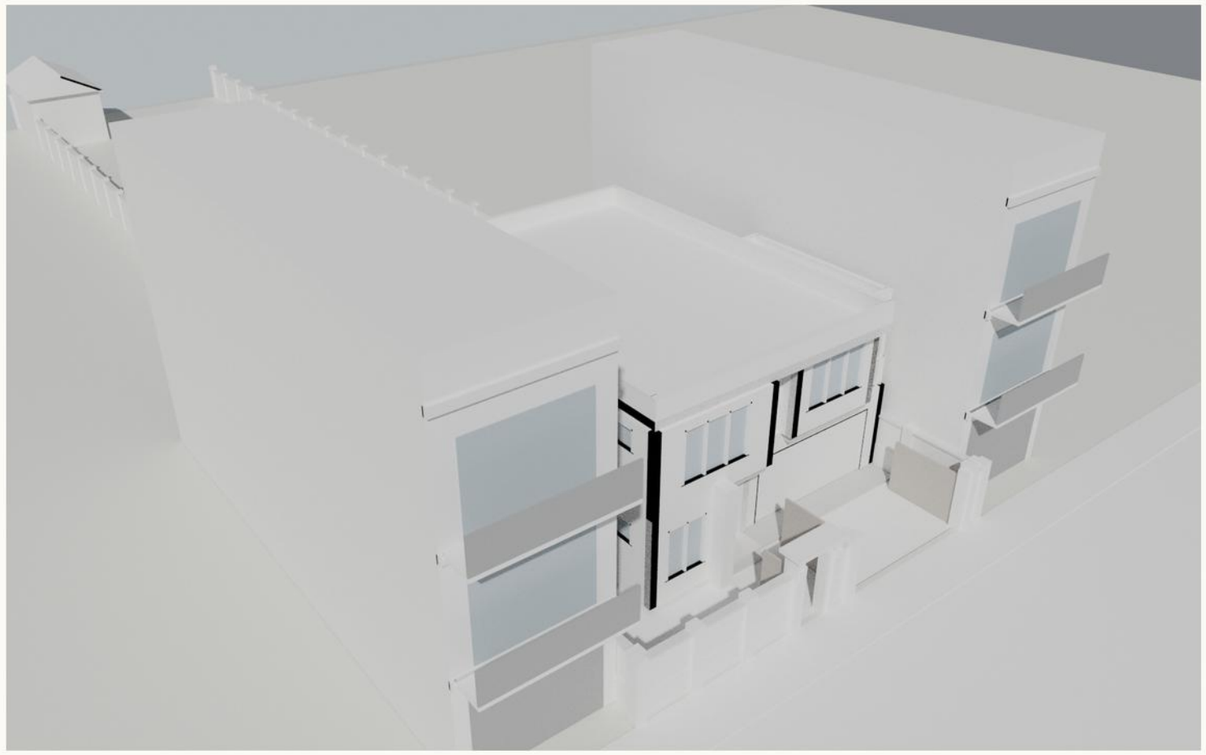

Clay massing


CONCEPT ONLY — NOT FOR CONSTRUCTION · subject to survey, legal merger, setbacks and permits

Walkthrough (Unity)

Interactive model: these are fixed viewpoints you can jump to with keys 1–9



Street

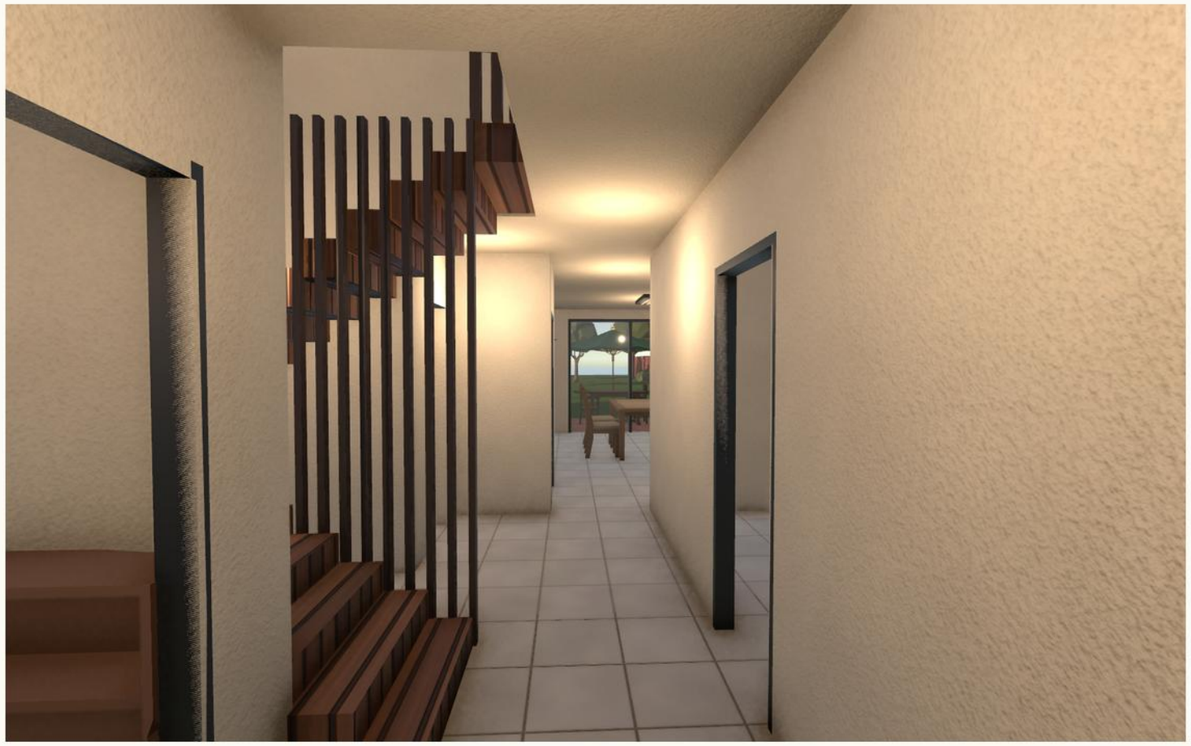

Foyer



Family



Kitchen

CONCEPT ONLY — NOT FOR CONSTRUCTION · subject to survey, legal merger, setbacks and permits

Walkthrough (Unity)

Interactive model: these are fixed viewpoints you can jump to with keys 1–9



Garage



Rumpus



Bed1




Deck


CONCEPT ONLY — NOT FOR CONSTRUCTION · subject to survey, legal merger, setbacks and permits

Walkthrough (Unity)

Interactive model: these are fixed viewpoints you can jump to with keys 1–9

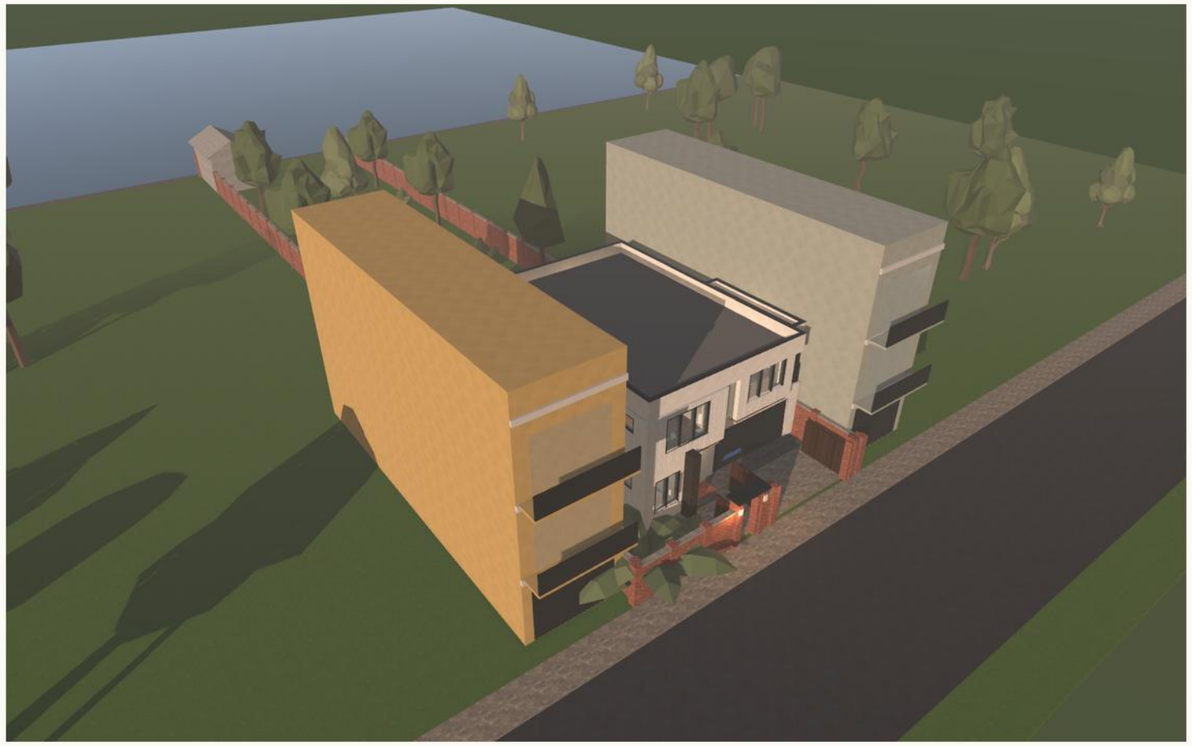


Aerial

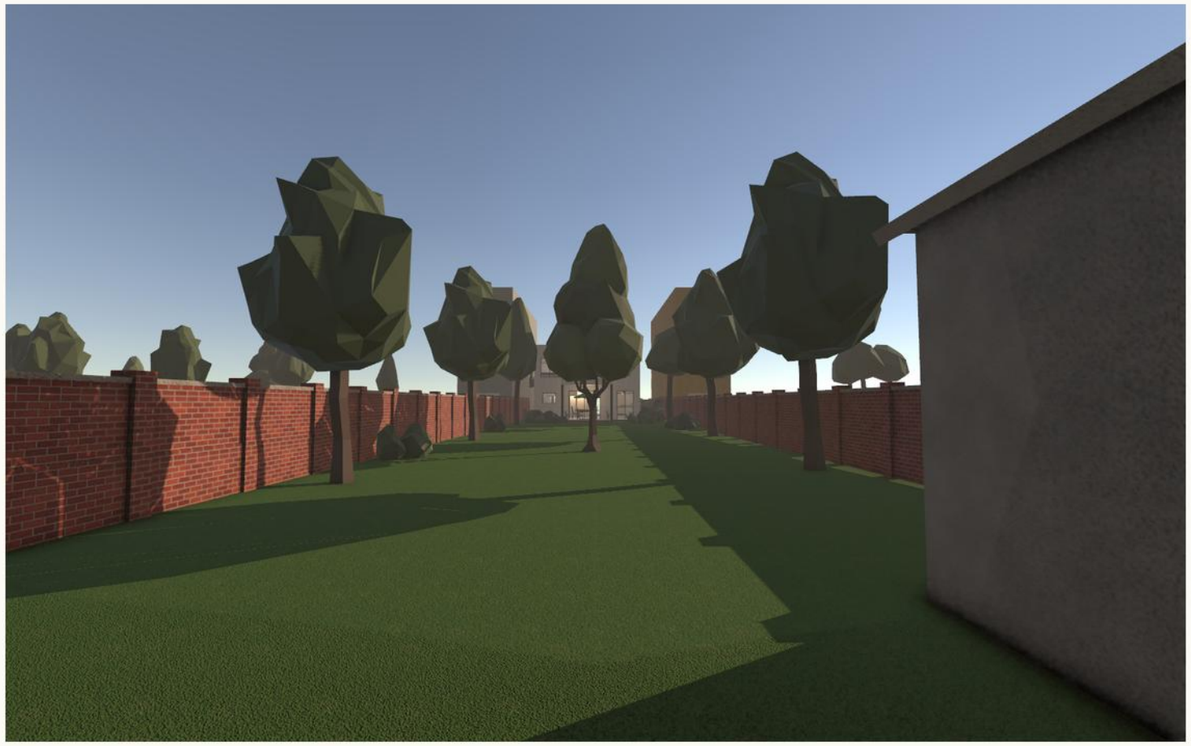

Riverside



Dollhouse Ground

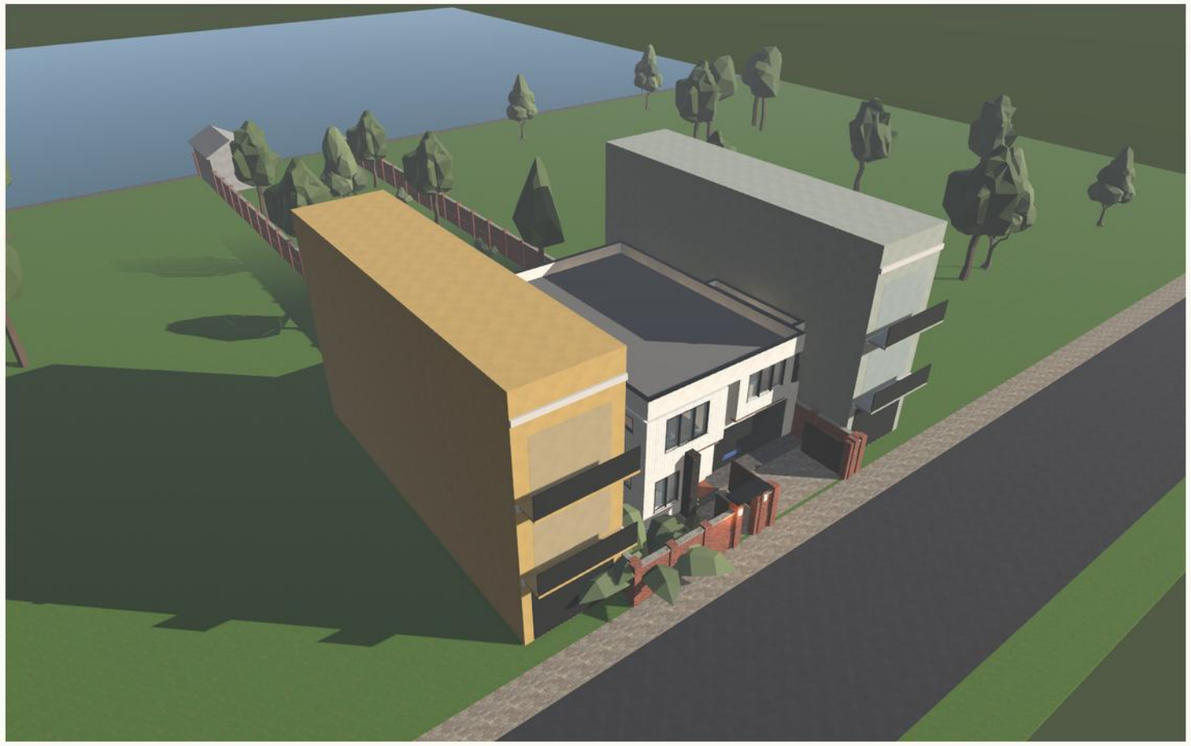

Sun study: winter solstice, 09:00 solar time

CONCEPT ONLY — NOT FOR CONSTRUCTION · subject to survey, legal merger, setbacks and permits

Walkthrough (Unity)


Interactive model: these are fixed viewpoints you can jump to with keys 1–9




Sun study: winter solstice, 12:00 solar time



Sun study: winter solstice, 15:00 solar time

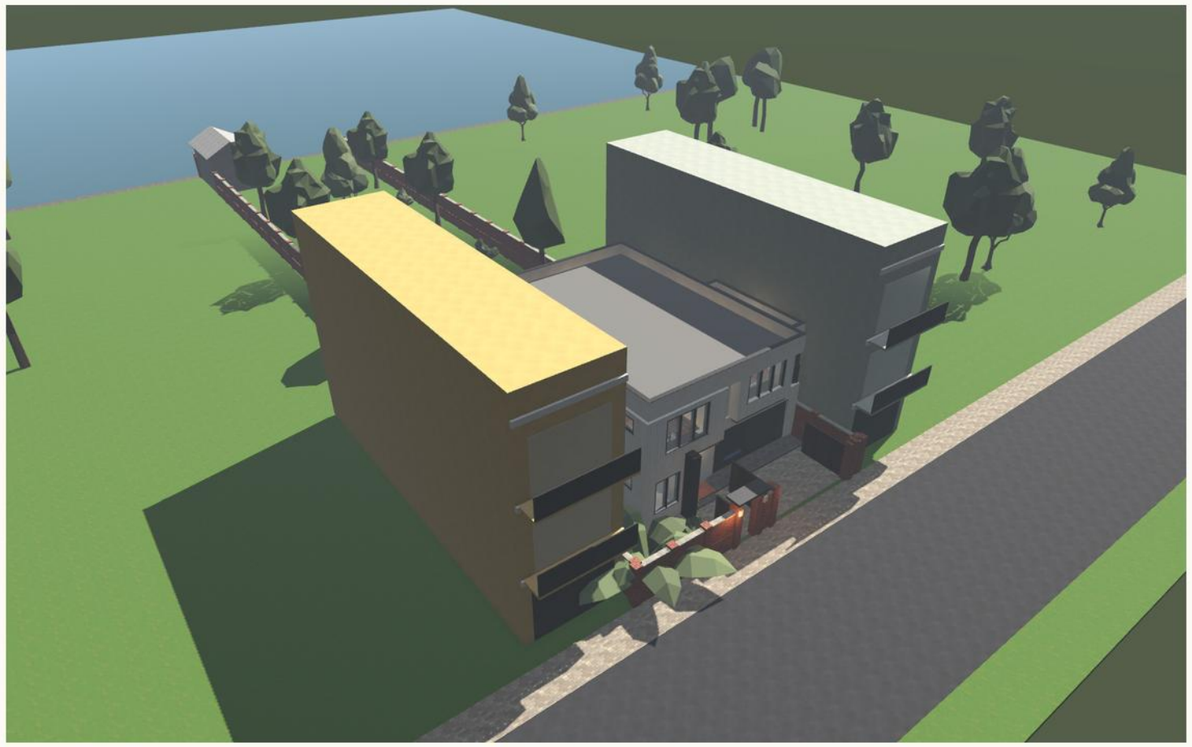

Sun study: summer solstice, 09:00 solar time

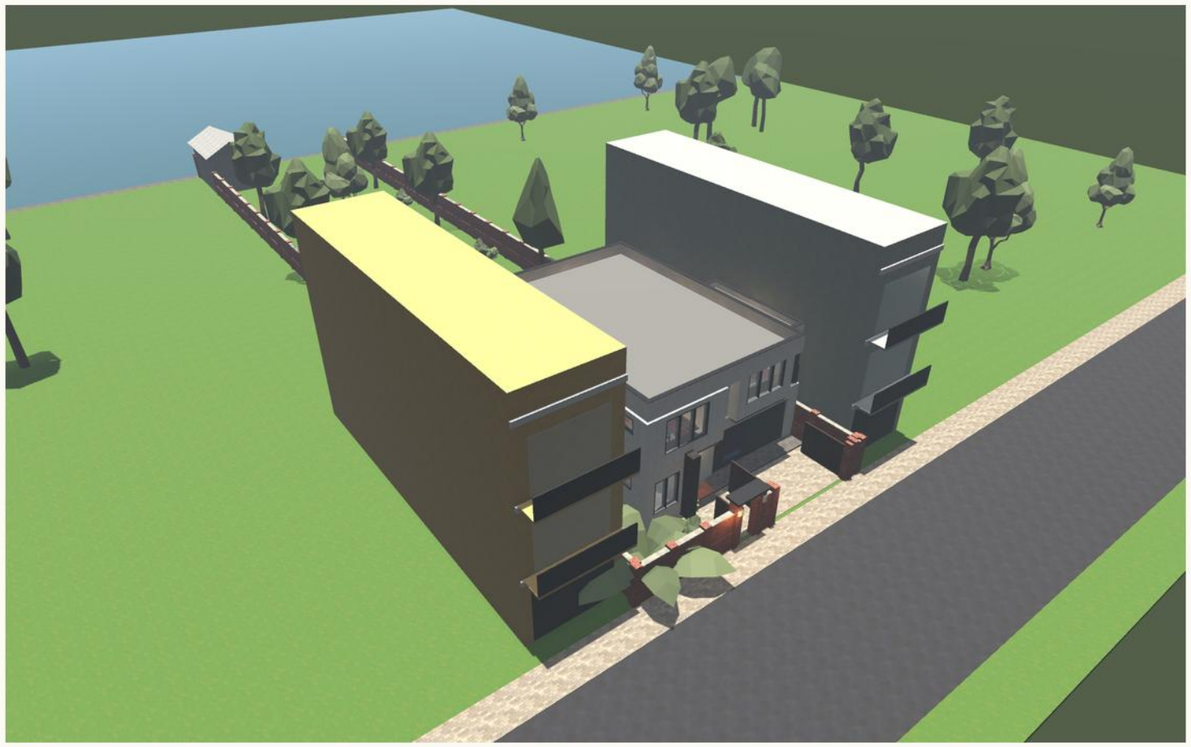


Sun study: summer solstice, 12:00 solar time

CONCEPT ONLY — NOT FOR CONSTRUCTION · subject to survey, legal merger, setbacks and permits

Walkthrough (Unity)

Interactive model: these are fixed viewpoints you can jump to with keys 1–9

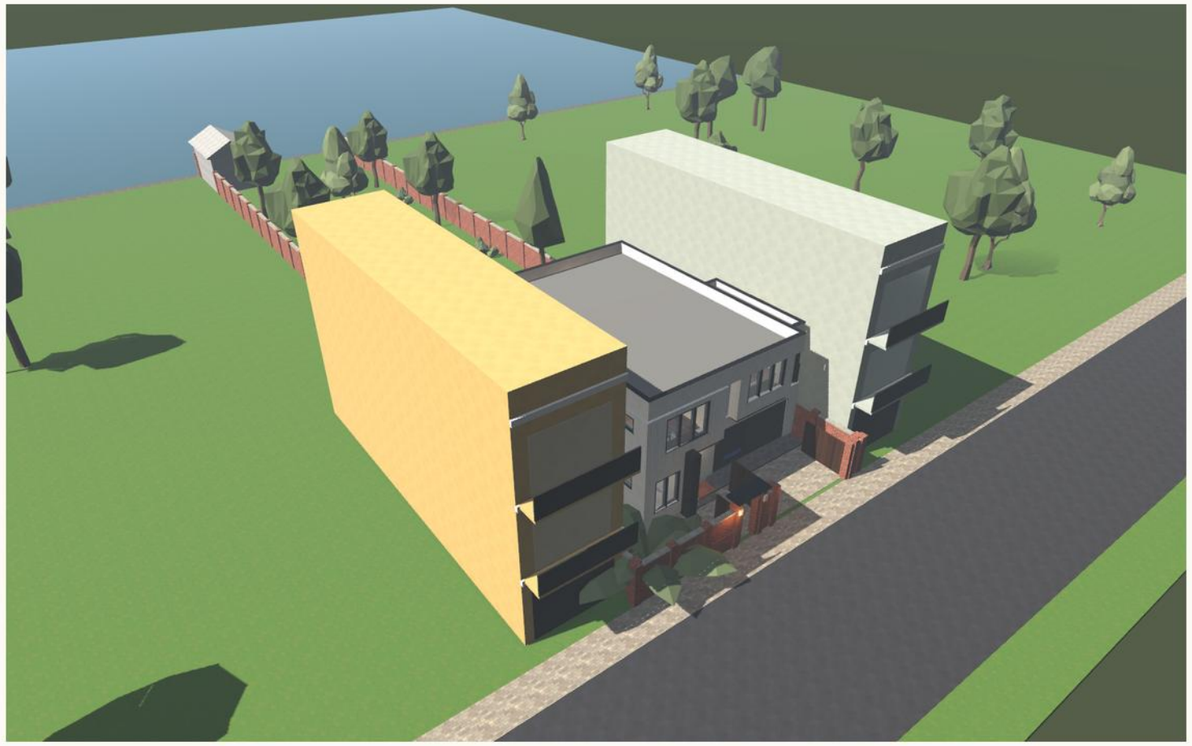

Sun study: summer solstice, 15:00 solar time

CONCEPT ONLY — NOT FOR CONSTRUCTION · subject to survey, legal merger, setbacks and permits